GROUND FLOOR PLAN (LEVEL 01)

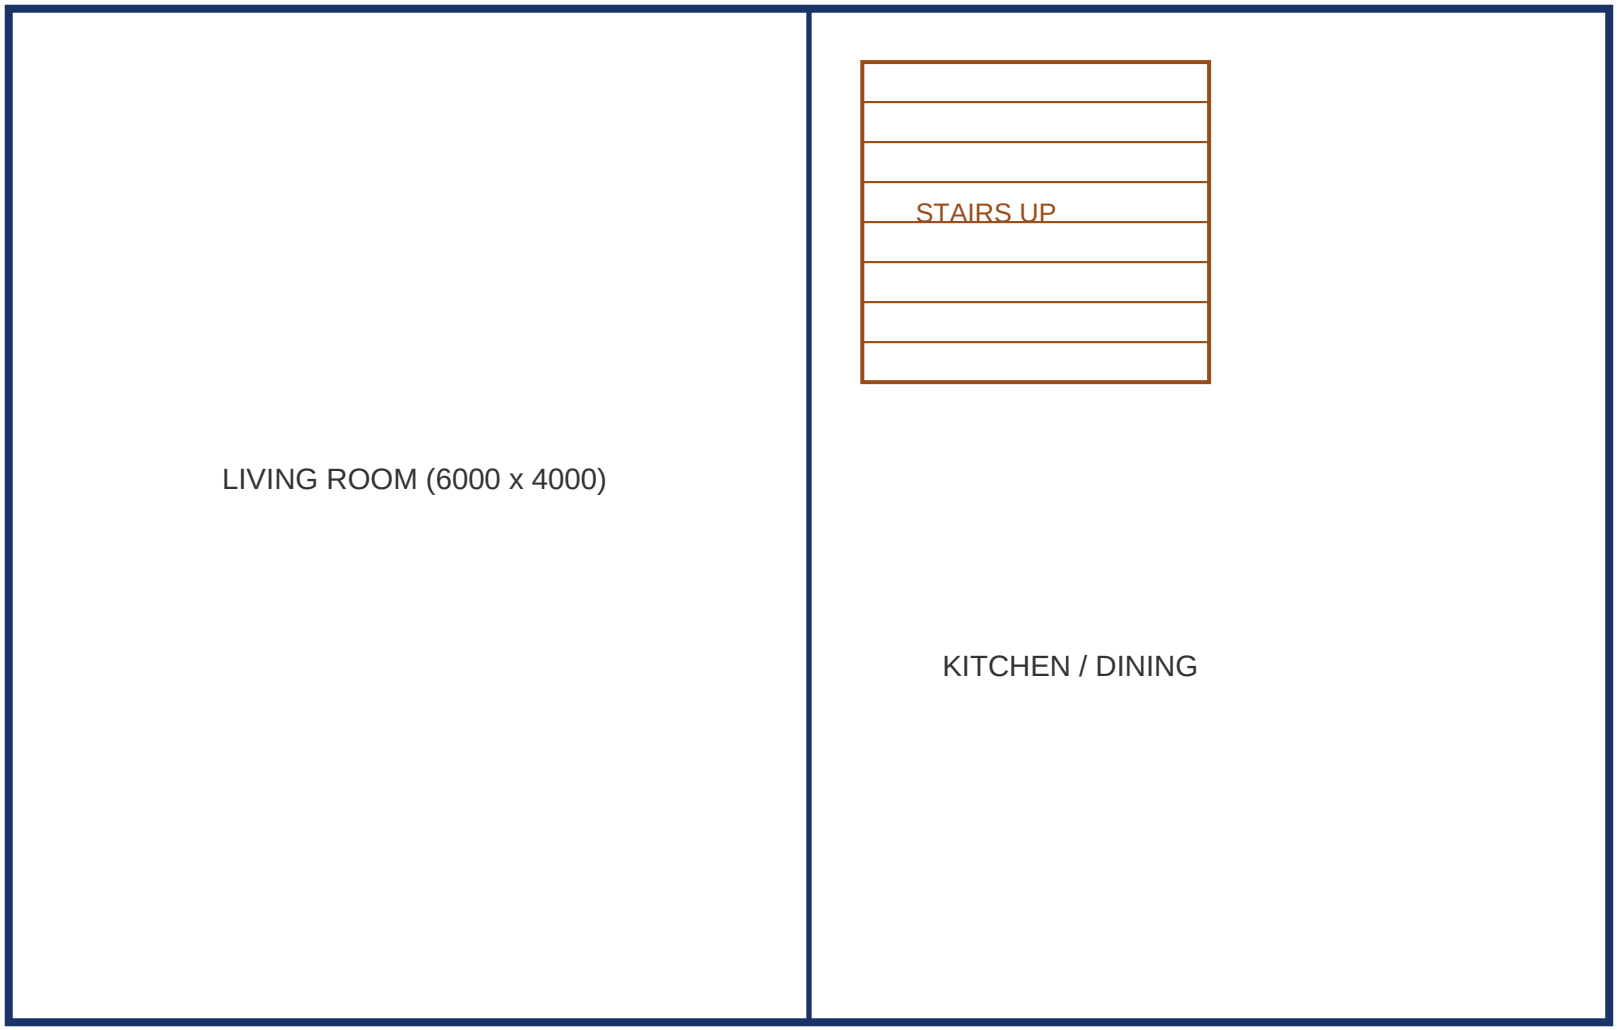

FIRST FLOOR PLAN (LEVEL 02)

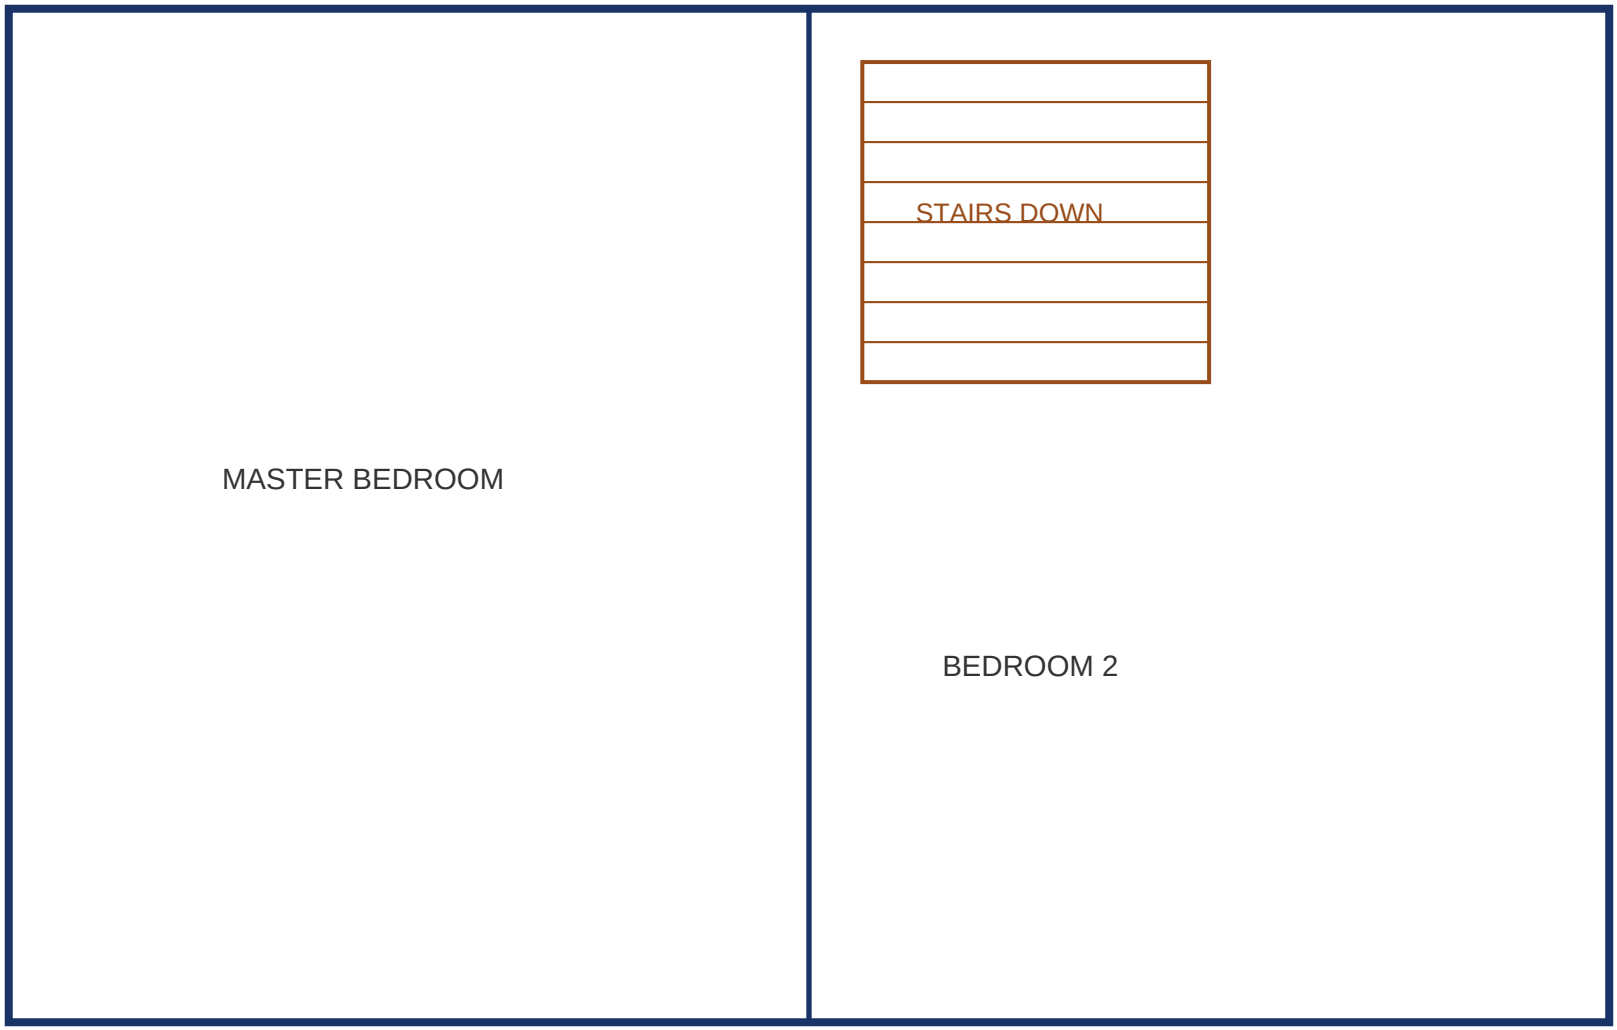

8000 mm (WIDTH)